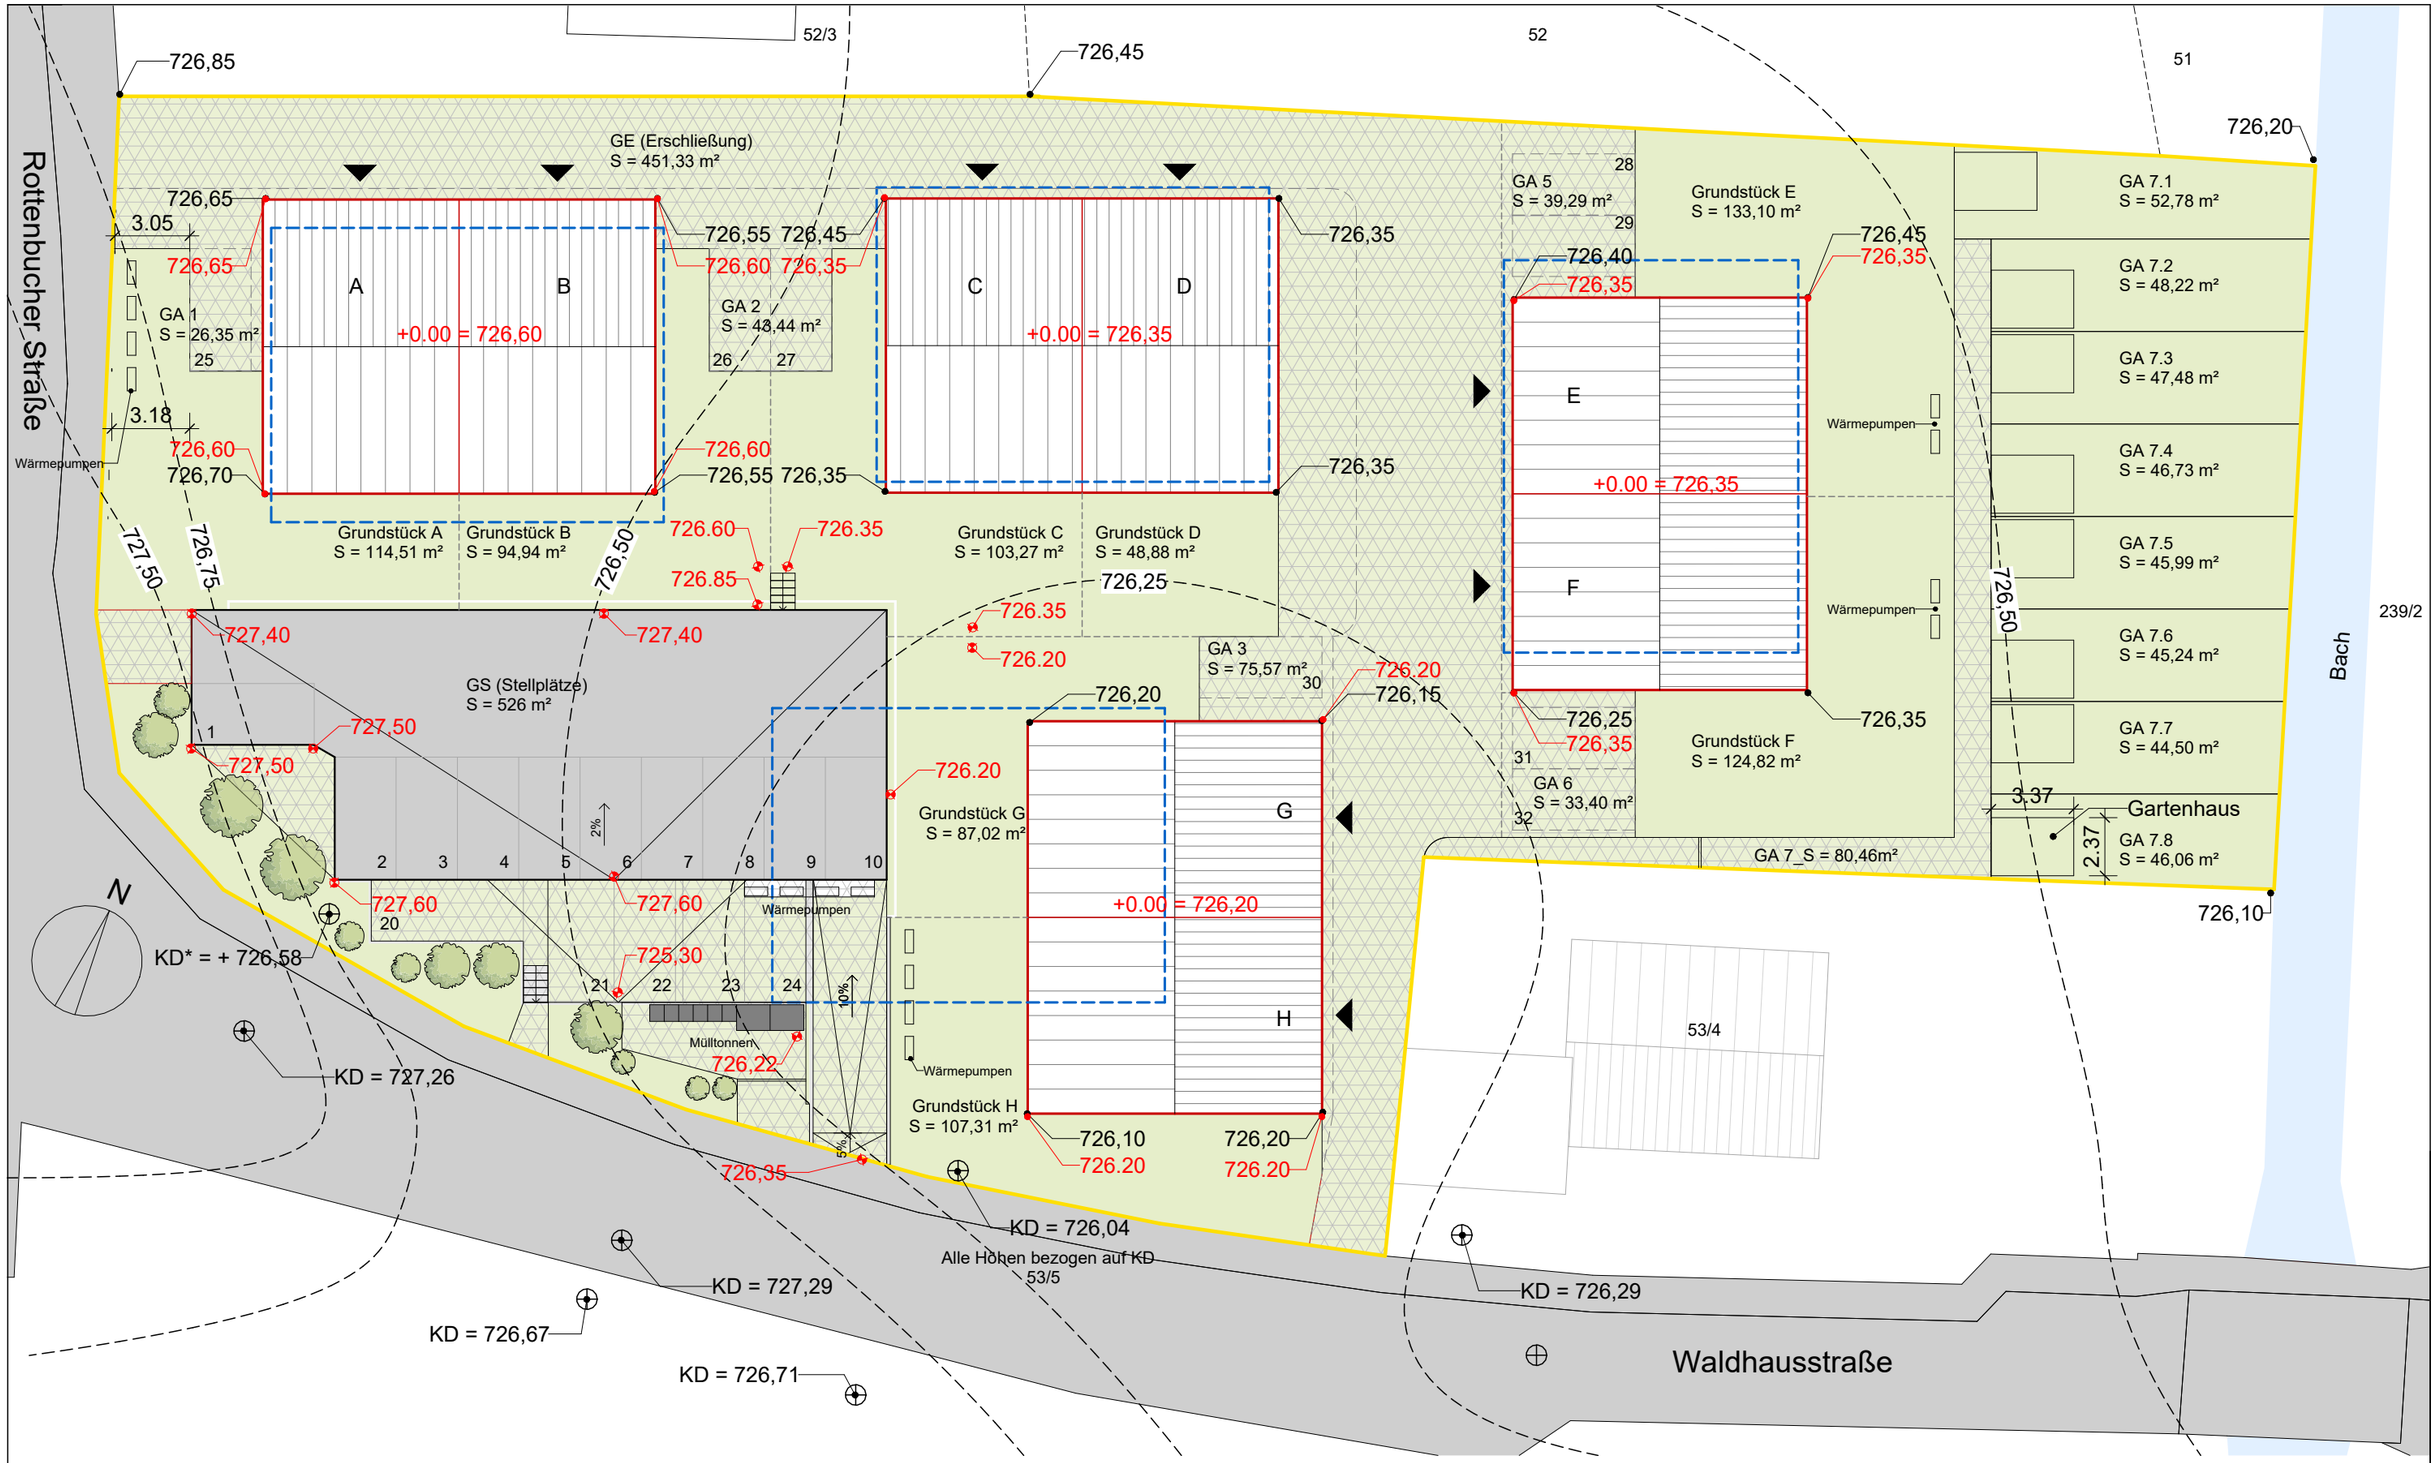


Legende

- Asphalt, Beton
- Rasengitterstein, Pflastersteine wasserdurchlässig
- Rasen
- Baugrenze laut dem Bebauungsplan
- Geplante Bebauung
- Grundstückgrenze
- KD - Kanaldeckel
- 726,10 Höhen µ.NN Bestand
- 726,10 Höhen µ.NN Planung

Projekt: **Abbruch des Bestandes und Neubau von vier Doppelhäusern** Rottenbucher Straße 35, 87662 Osterzell	Maßstab: 1 : 250	Größe: 420 x 297	Stand: 21.10.2026
Bauherr: **Wohnen und Pflege GmbH** Fuchsbergstraße. 7, 83104 Tuntenhausen	Planname: Freiflächenplan		Plannummer: 2
Planer: **BPS Planung GmbH** Architekt Dimitri Kats Wilhelmine-Reichard-Str. 26, 80935 München Tel. +49 152 317 44 44 6 E: d.kats@bpsint.de	Plan-Nr.: 100OSZ_BPS_LP2_AR_L00_02		

Projekt ID	Planverfasser	Phase	Gewerk	Bauteil	Unter kategorie	Plantyp	Geschoss	Nr	Status	Index